


NYLON PRODUCTION & PACKAGING FACILITY

PLANNED FOR EFFICIENT FLOW, QUALITY & SUSTAINABLE OPERATIONS • 10.17m x 39.40m HALL • EAVES +8.0m / RIDGE +12.0m

GROUND FLOOR PLAN

SCALE INDICATIVE (see A102 for 1:100)

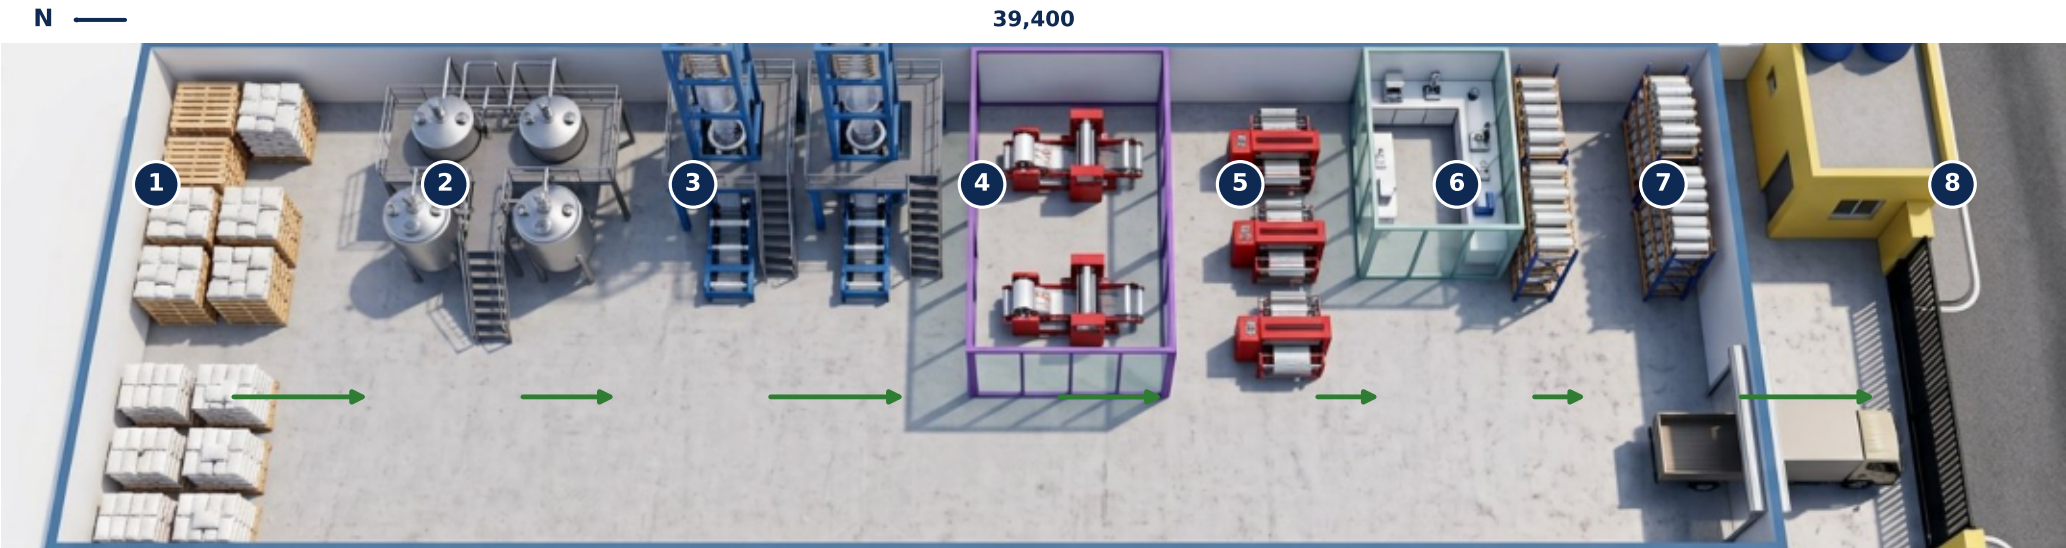

- 1
- 2
- 3
- 4
- 5
- 6
- 7
- 8
- RAW MATERIALS
STORE
- MIXING &
WEIGHING
- BLOWN-FILM
EXTRUSION
- FLEXO PRINTING
(WALLED)
- CUTTING &
HEAT-SEALING
- QUALITY CONTROL
LABORATORY
- FINISHED GOODS
STORE
- DISPATCH
& LOADING


UTILITY CORE (SOUTH END)

- GATEHOUSE + 4.6m SLIDING GATE
- SECURITY + LOBBY + STORE
- POWER ROOM + GENERATOR
- MEZZ UTILITIES + PANELS (U1)
- BOREHOLE → TANKS (GRAVITY)
- SEPTIC + SOAKAWAY (EAST)

CONTINUOUS RIDGE
VENTILATORS

TRANSLUCENT
SKYLIGHT STRIPS

PITCHED METAL ROOF
38° (8m → 12m)

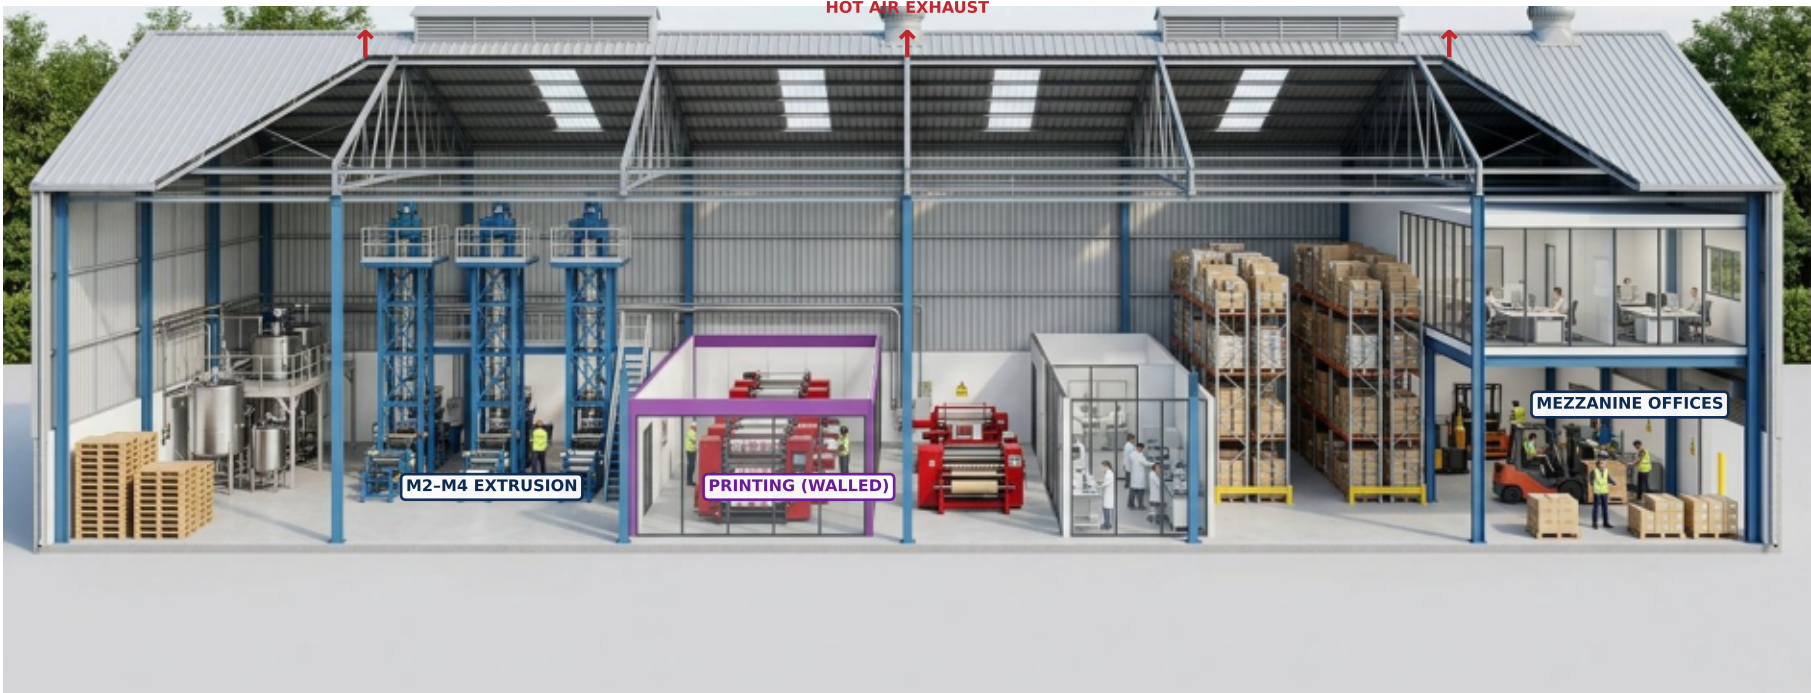

SIDE ELEVATION



CROSS SECTION B-B (through extrusion)



BUILDING & DESIGN DATA

TOTAL SIZE	39.40 × 10.17m
EAVE HEIGHT	8.0m
RIDGE HEIGHT	12.0m
MEZZANINE	+4.0m (95.6m²)
STRUCTURE	STEEL PORTAL @6m
ROOF	METAL + SKYLIGHTS
VENTILATION	RIDGE VENTS
FLOOR	POWER-FLOAT
FIRE	HOSE REELS + EXT.

LEGEND - PRODUCTION FLOW

- 1
- 2
- 3
- 4
- 5
- 6
- 7
- 8
- RAW MATERIALS
STORE
- MIXING &
WEIGHING
- BLOWN-FILM
EXTRUSION
- FLEXO PRINTING (WALLED)
- CUTTING & HEAT-SEALING
- QUALITY CONTROL LAB
- FINISHED GOODS
STORE
- DISPATCH & LOADING

FLOW →