


NYLON PRODUCTION & PACKAGING FACILITY

PLANNED FOR EFFICIENT FLOW, QUALITY & SUSTAINABLE OPERATIONS • 10.17m x 39.40m HALL • EAVES +8.0m / RIDGE +12.0m

GROUND FLOOR PLAN

SCALE INDICATIVE (see A102 for 1:100)

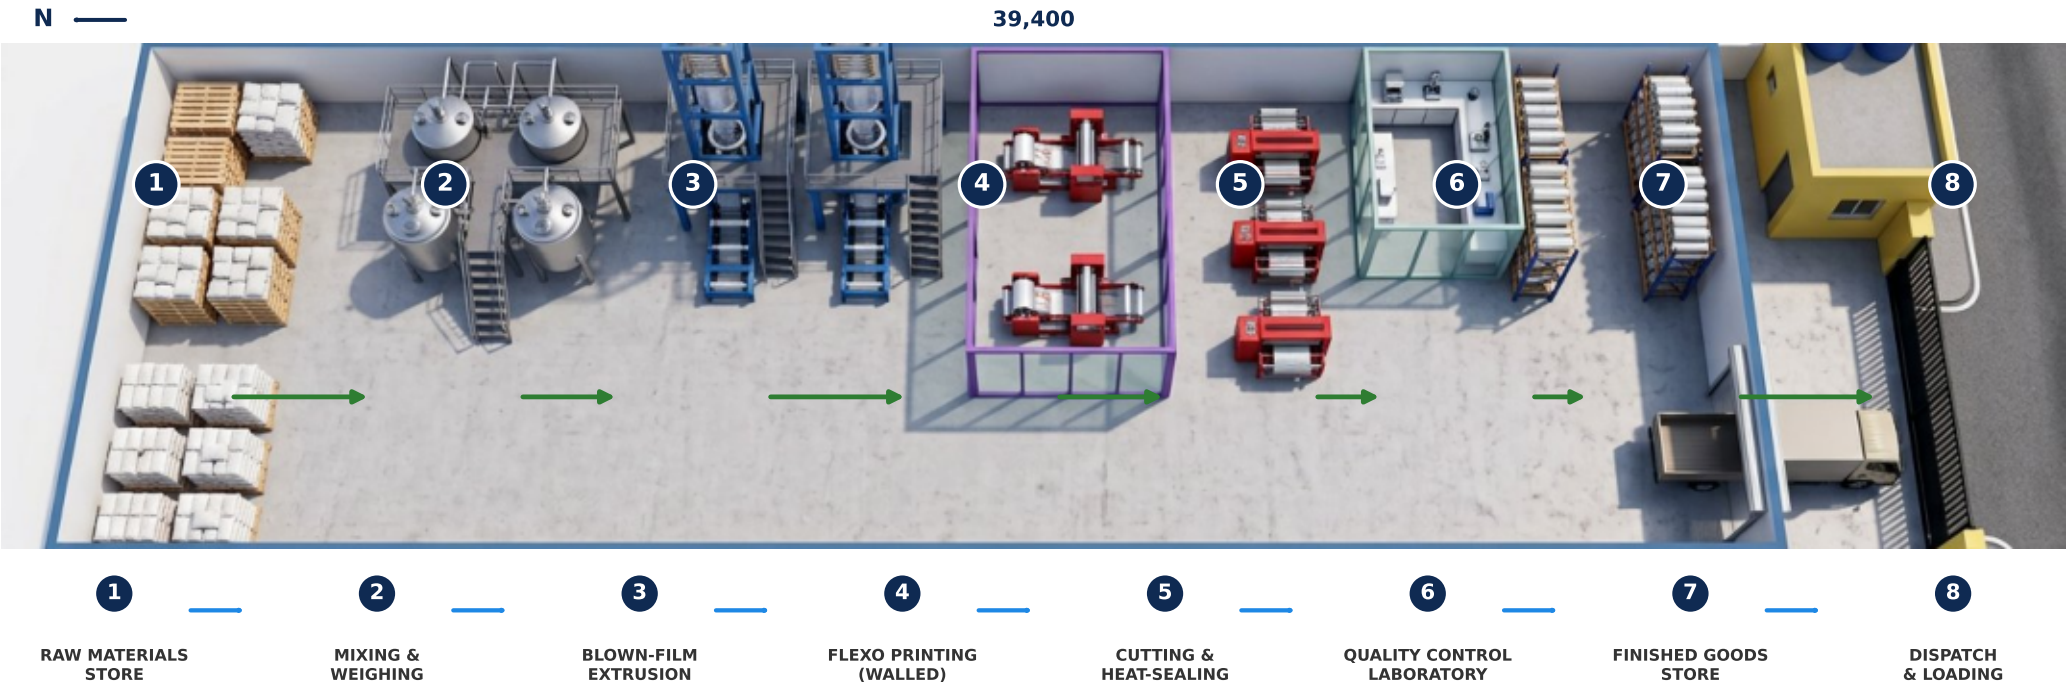


UTILITY CORE (SOUTH END)

- GATEHOUSE + 4.6m SLIDING GATE
- SECURITY + LOBBY + STORE
- POWER ROOM + GENERATOR
- MEZZ UTILITIES + PANELS (U1)
- BOREHOLE → TANKS (GRAVITY)
- SEPTIC + SOAKAWAY (EAST)

CONTINUOUS RIDGE VENTILATORS

TRANSLUCENT SKYLIGHT STRIPS

PITCHED METAL ROOF 38° (8m → 12m)

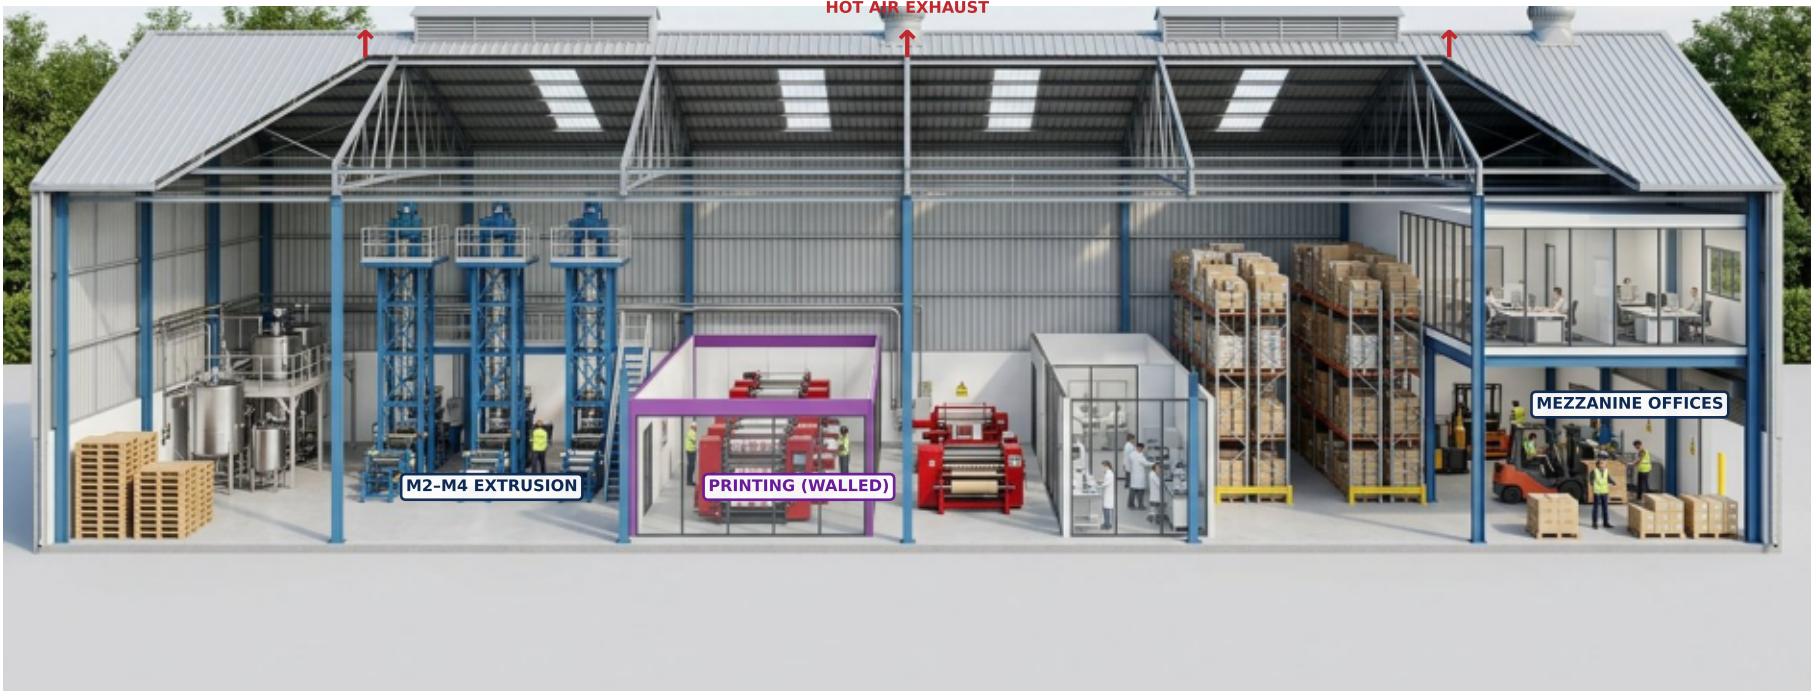

MEZZANINE OFFICES + DISPATCH (SOUTH)

WALLED PRINTING ROOM (chemicals, own entry E4)

STEEL PORTAL @6.0m 7 FRAMES, 39.40m

SIDE ELEVATION



CROSS SECTION B-B (through extrusion)



BUILDING & DESIGN DATA

TOTAL SIZE	39.40 × 10.17m
EAVE HEIGHT	8.0m
RIDGE HEIGHT	12.0m
MEZZANINE	+4.0m (95.6m²)
STRUCTURE	STEEL PORTAL @6m
ROOF	METAL + SKYLIGHTS
VENTILATION	RIDGE VENTS
FLOOR	POWER-FLOAT
FIRE	HOSE REELS + EXT.

LEGEND - PRODUCTION FLOW


- 1 RAW MATERIALS STORE
- 2 MIXING & WEIGHING
- 3 BLOWN-FILM EXTRUSION
- 4 FLEXO PRINTING (WALLED)
- 5 CUTTING & HEAT-SEALING
- 6 QUALITY CONTROL LAB
- 7 FINISHED GOODS STORE
- 8 DISPATCH & LOADING

FLOW →

NYLON PRODUCTION & PACKAGING PLANT

Quality Packaging for a Sustainable Future • Ilogbo / Foundation Road, Oko-Afo, Badagry, Lagos

GROUND FLOOR PLAN (Production hall 39.40 × 10.17m — N on left)

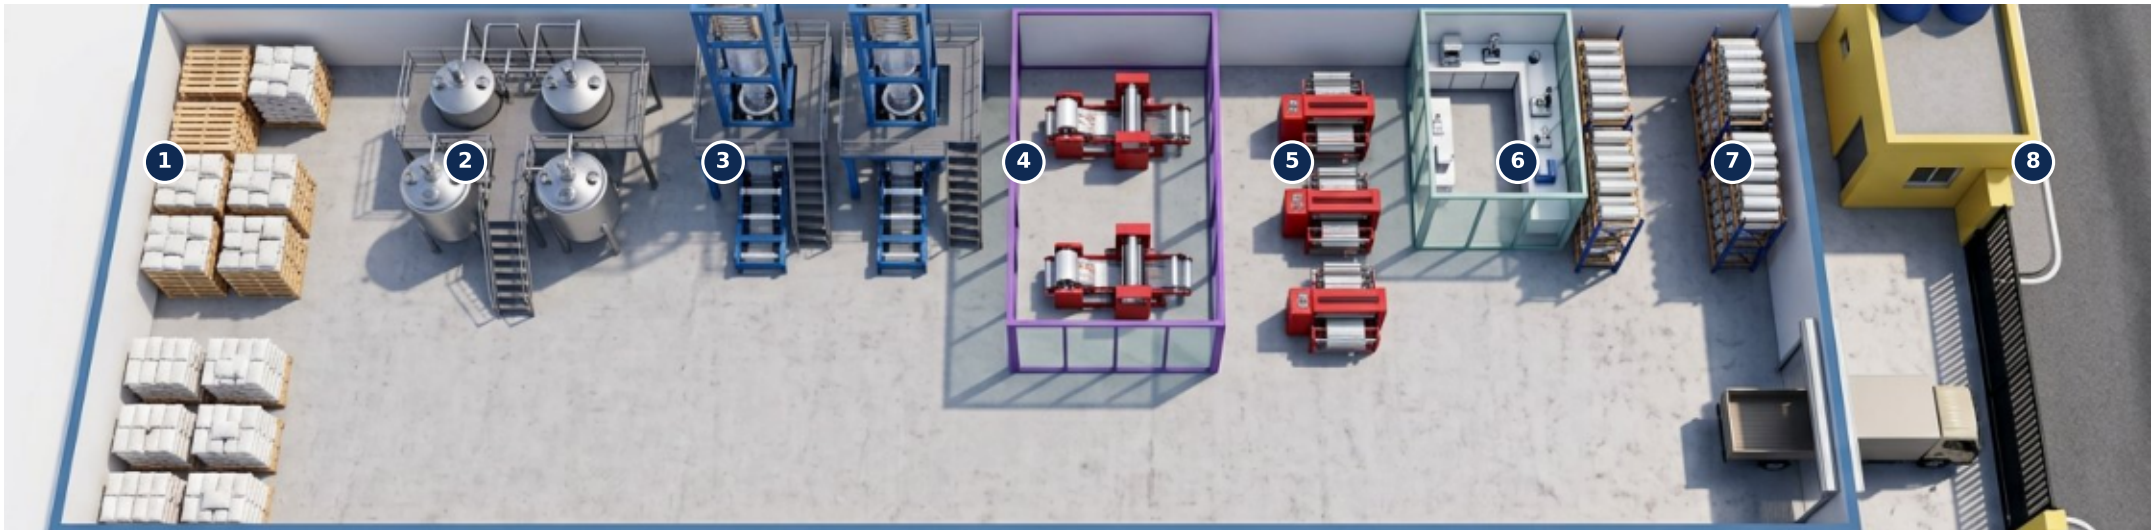

FRONT ELEVATION (south, from main road)




RIGHT SIDE ELEVATION (east, 39.40m)



LONGITUDINAL SECTION (A-A, indicative)



3D CUTAWAY VIEW (without roof)

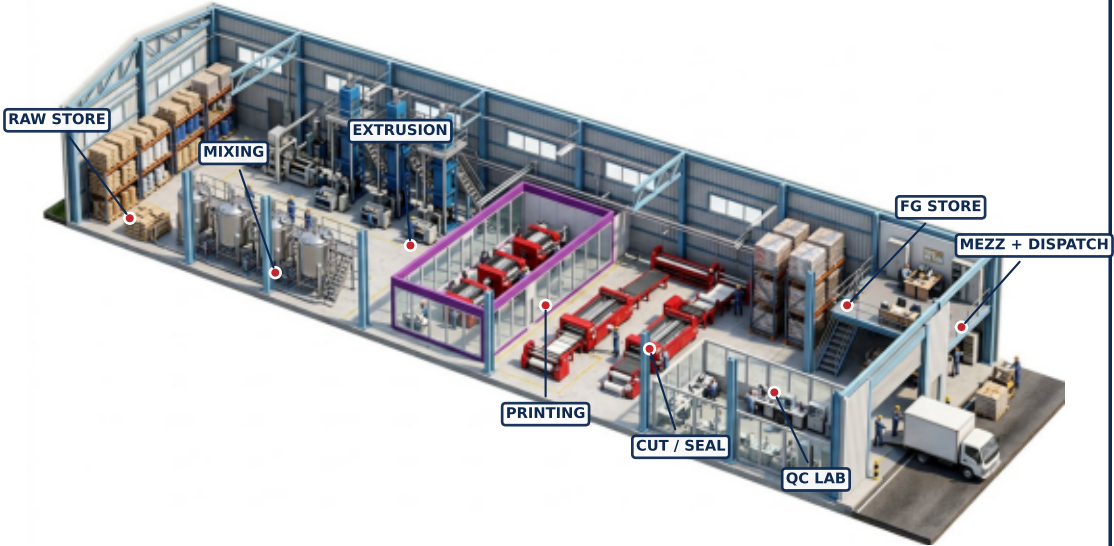

CROSS SECTION B-B (indicative)



AERIAL VIEW (from main road — gate + tanks)



KEY FEATURES

- ✓ Linear N→S production flow
- ✓ Walled print room + own entry
- ✓ Mezz offices + utilities
- ✓ Skylights + ridge ventilation
- ✓ Decked gate/power + tanks

MACHINE / AREA LIST

- M1 Mixing / Weighing
- M2-M4 Blown-film extrusion
- M5-M6 Flexo printing (walled)
- M7-M9 Cutting / Heat-seal
- M10 QC bench • M11 Granulator
- Raw / QC / FG stores • Dispatch

FLOOR SUMMARY

Plot	806.9 m ²
Production G/F	400.7 m ²
Mezzanine	95.6 m ²
Gate / Power	27.6 m ²
Total GFA	523.9 m ²
Eaves / Ridge	+8.0 / +12.0m