


SITE PLAN — 806.896 m² (LAA/195/29/2025/LA)

Production hall 10.17 × 39.40m • Gate/Security/Power block decked • Steel portal @6.0m • Eaves +8.0m / Ridge +12.0m

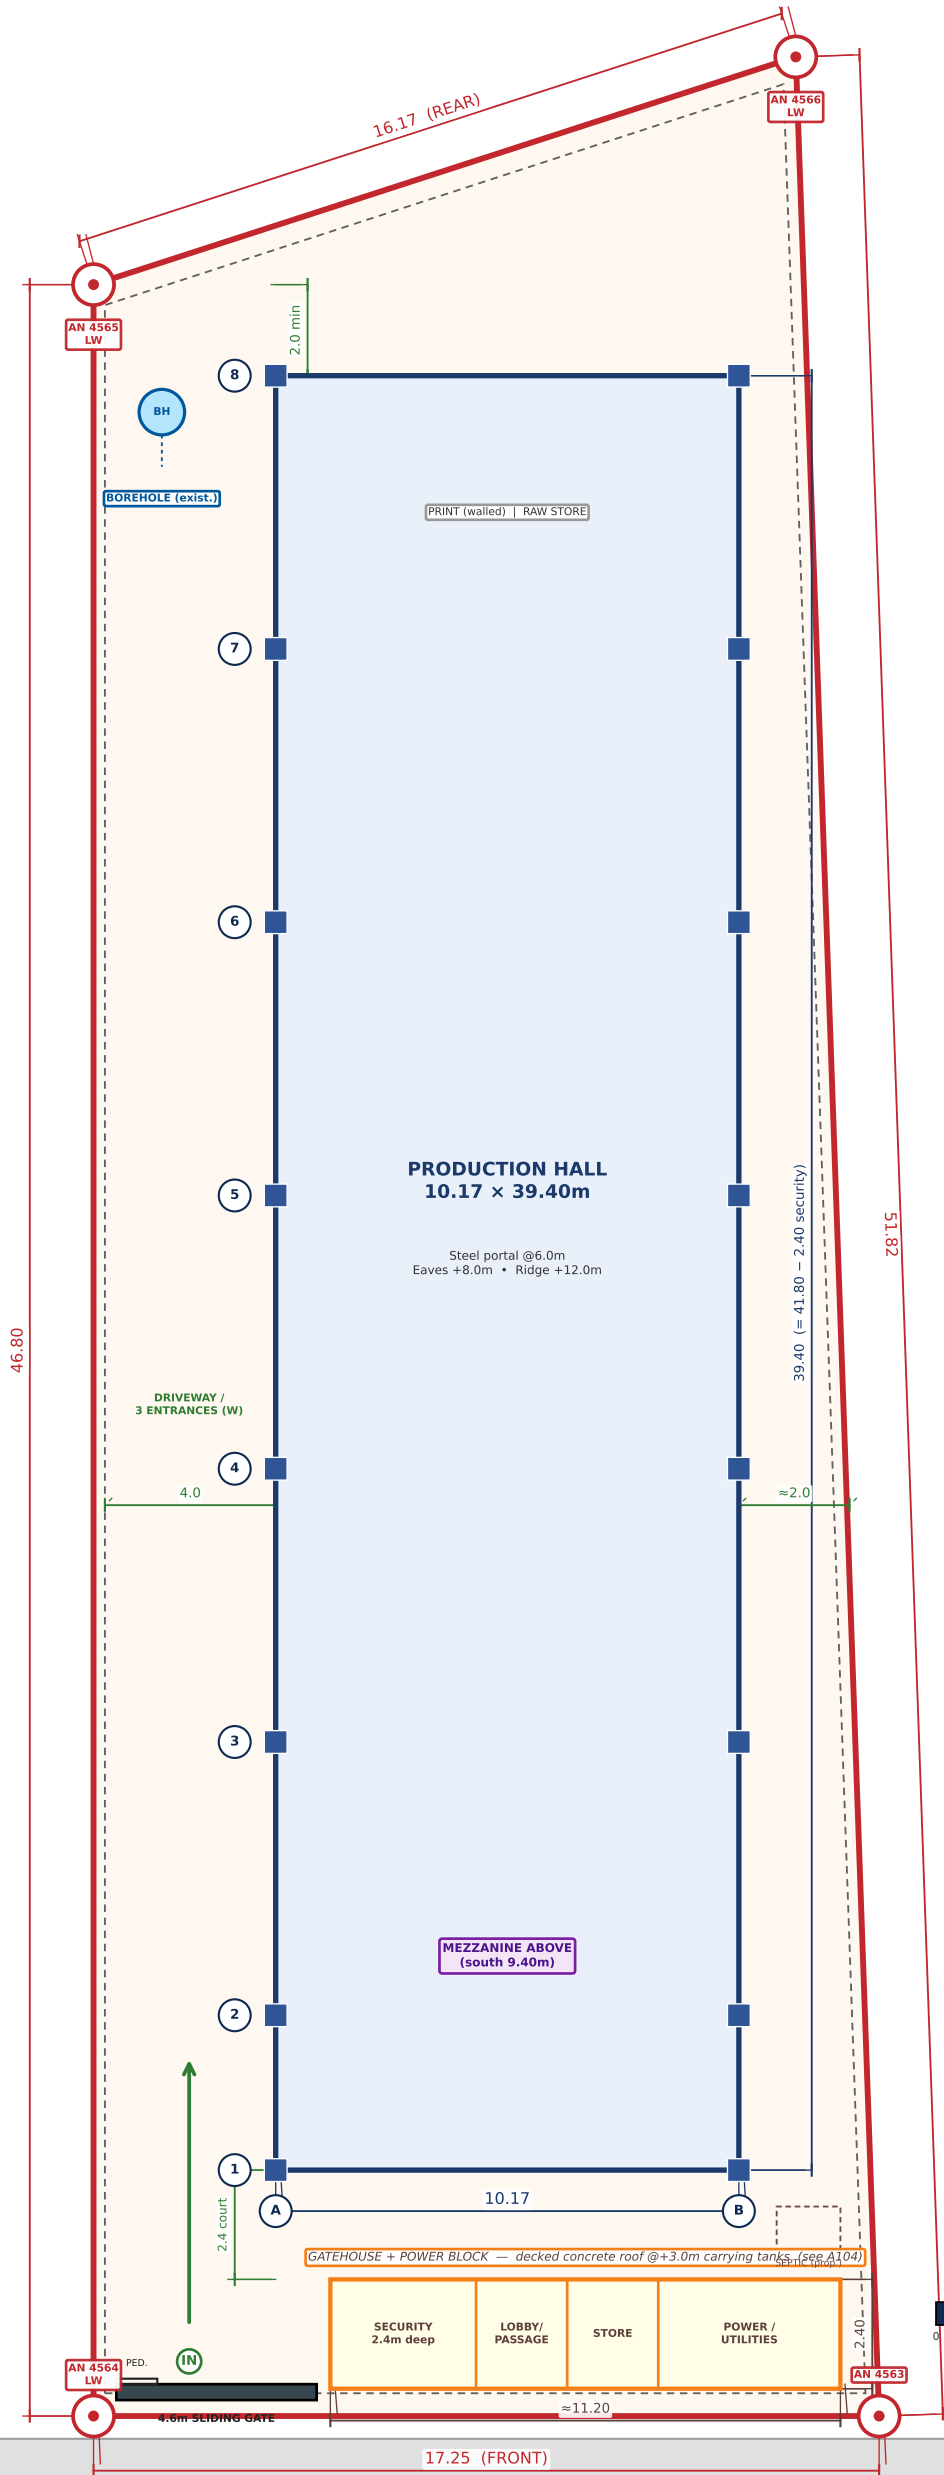

LEGEND

- Plot boundary
- Production walls
- Steel stanchion
- Gate / power block
- Flow / driveway

SITE NOTES & AREAS

- RED line = plot boundary (survey).
- BLUE = production walls + steel stanchions @6.0m c/c.
- Production shortened 2.40m to allow gate/security/power block.
- West driveway 4.0m: 3 entrances (Raw store / QC / Reception).
- Printing room walled + own east entrance (chemicals).
- Mezzanine over south 9.40m; decked for offices + utilities.
- Gate/power decked @+3.0m for 2× water tanks + header.
- Eaves +8.0m, ridge +12.0m; skylights + ridge vents.
- Borehole retained (NW).
- All dims in metres; verify on site.

AREA SCHEDULE

Plot	806.90 m²
Production G/F	400.70 m²
Mezzanine	95.60 m²
Gate/Power	27.60 m²
Total GFA	523.90 m²
Coverage	49.7%

SCALE BAR (m)



Main Gate → 4.6m sliding gate + pedestrian gate

ILOGBO / FOUNDATION ROAD (MAIN ROAD)

NYLON PRODUCTION & PACKAGING PLANT

Along Ilogbo / Foundation Road, Oko-Afo, Badagry LGA, Lagos State

A101 | SITE & LOCATION PLAN • GATEHOUSE • SETBACKS

1:200 (SITE) | 27-09-2026

PRELIMINARY - FOR DISCUSSION