


MEZZANINE FLOOR PLAN @+4.00m — OVER SOUTH 9.40m (95.6 m²)

Decked RC slab on steel beams • Offices + Staff + WCs + Utilities • Gallery overlooking hall • External fire-escape stair (E)

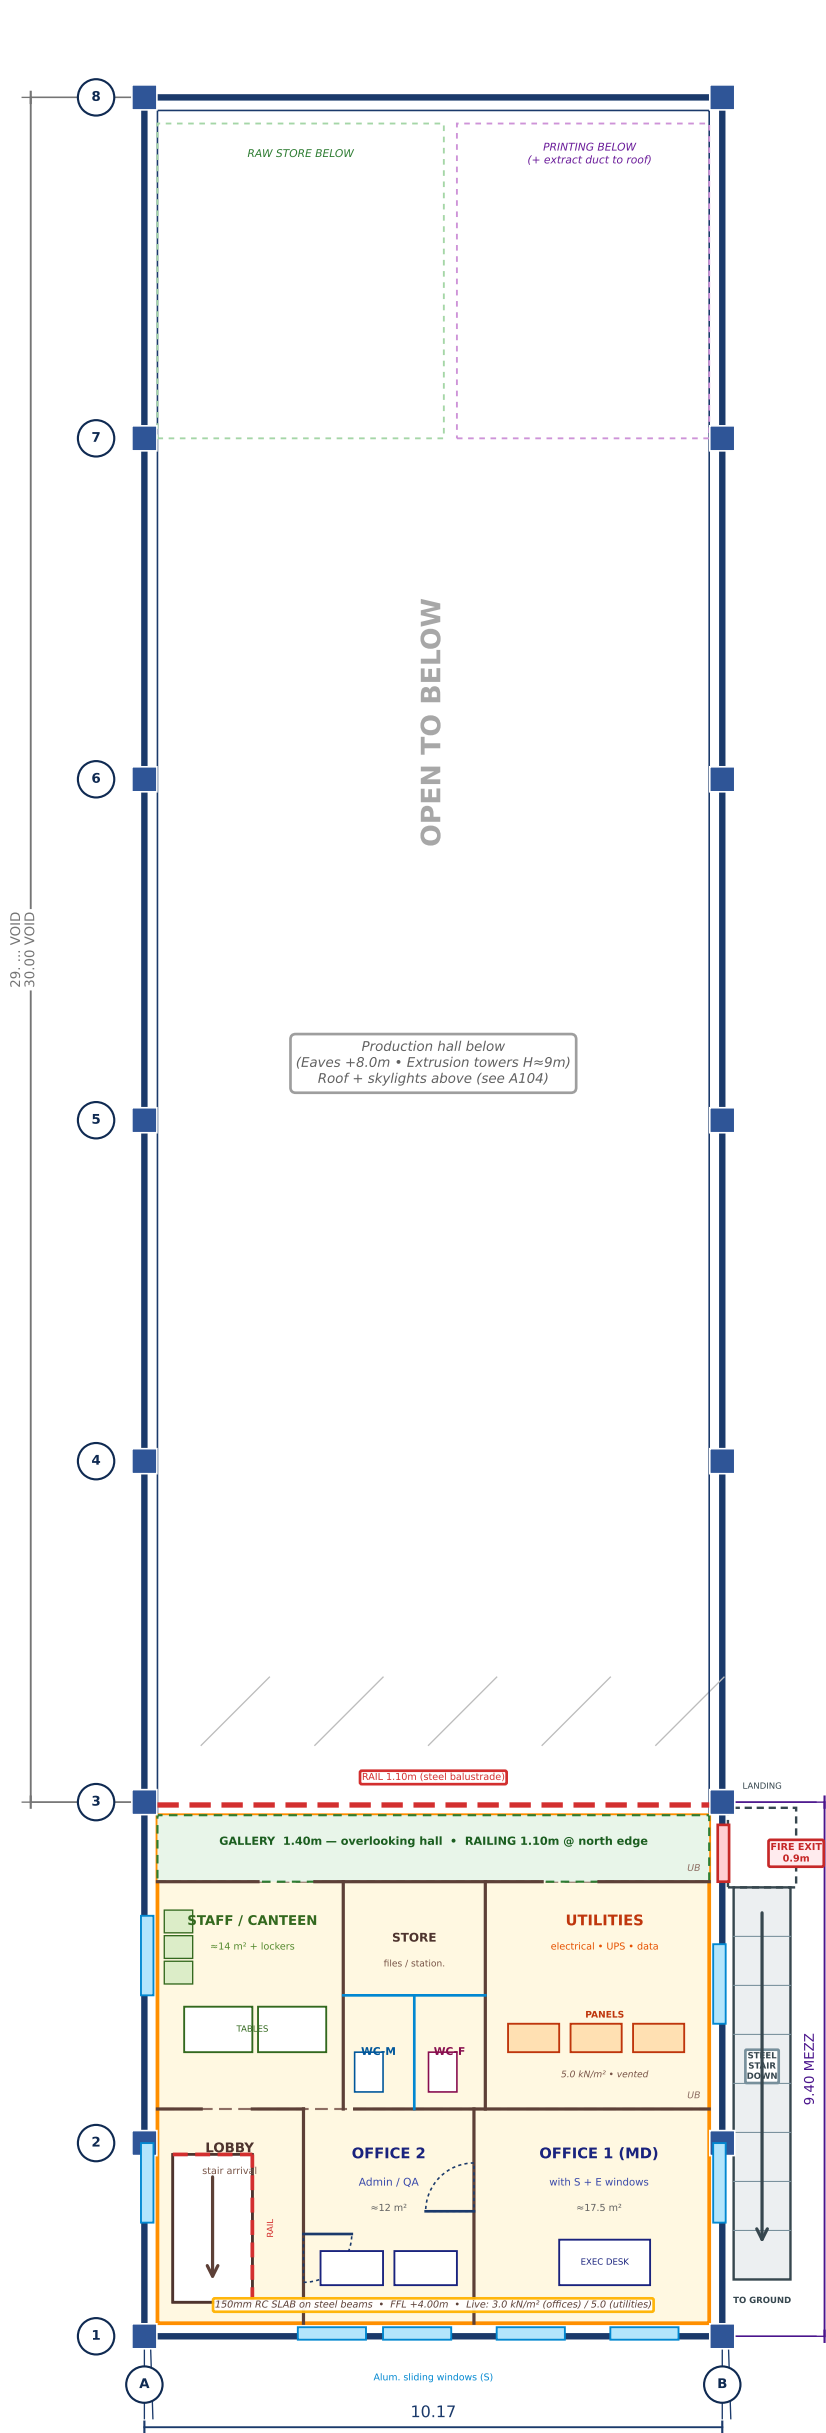

MEZZ AREAS	
Lobby/Stair	≈11 m²
Office 1 MD	≈17.5 m²
Office 2	≈12 m²
Staff	≈14 m²
WCs+Store	≈10 m²
Utilities	≈16.5 m²
Gallery	≈14 m²
TOTAL	≈95.6 m²

- MEZZ NOTES
- Slab 150 RC + screed,
 - steel UB/APFC beams.
 - Headroom: 4.0 below,
 - 4.0 to eaves above.
 - Railing 1.10m steel.
 - Stair 1.20 wide, 2 flights,
 - riser ≈175, going 250.
 - Fire exit E + external
 - steel stair to ground.
 - Offices: AC + data,
 - 337lux; Utilities vented.
 - WC soil to septic (E).
 - Verify structure with
 - engineer before build.