


ROOF PLAN — GABLE EAVES +8.00m • RIDGE +12.00m (RISE 4.00m)

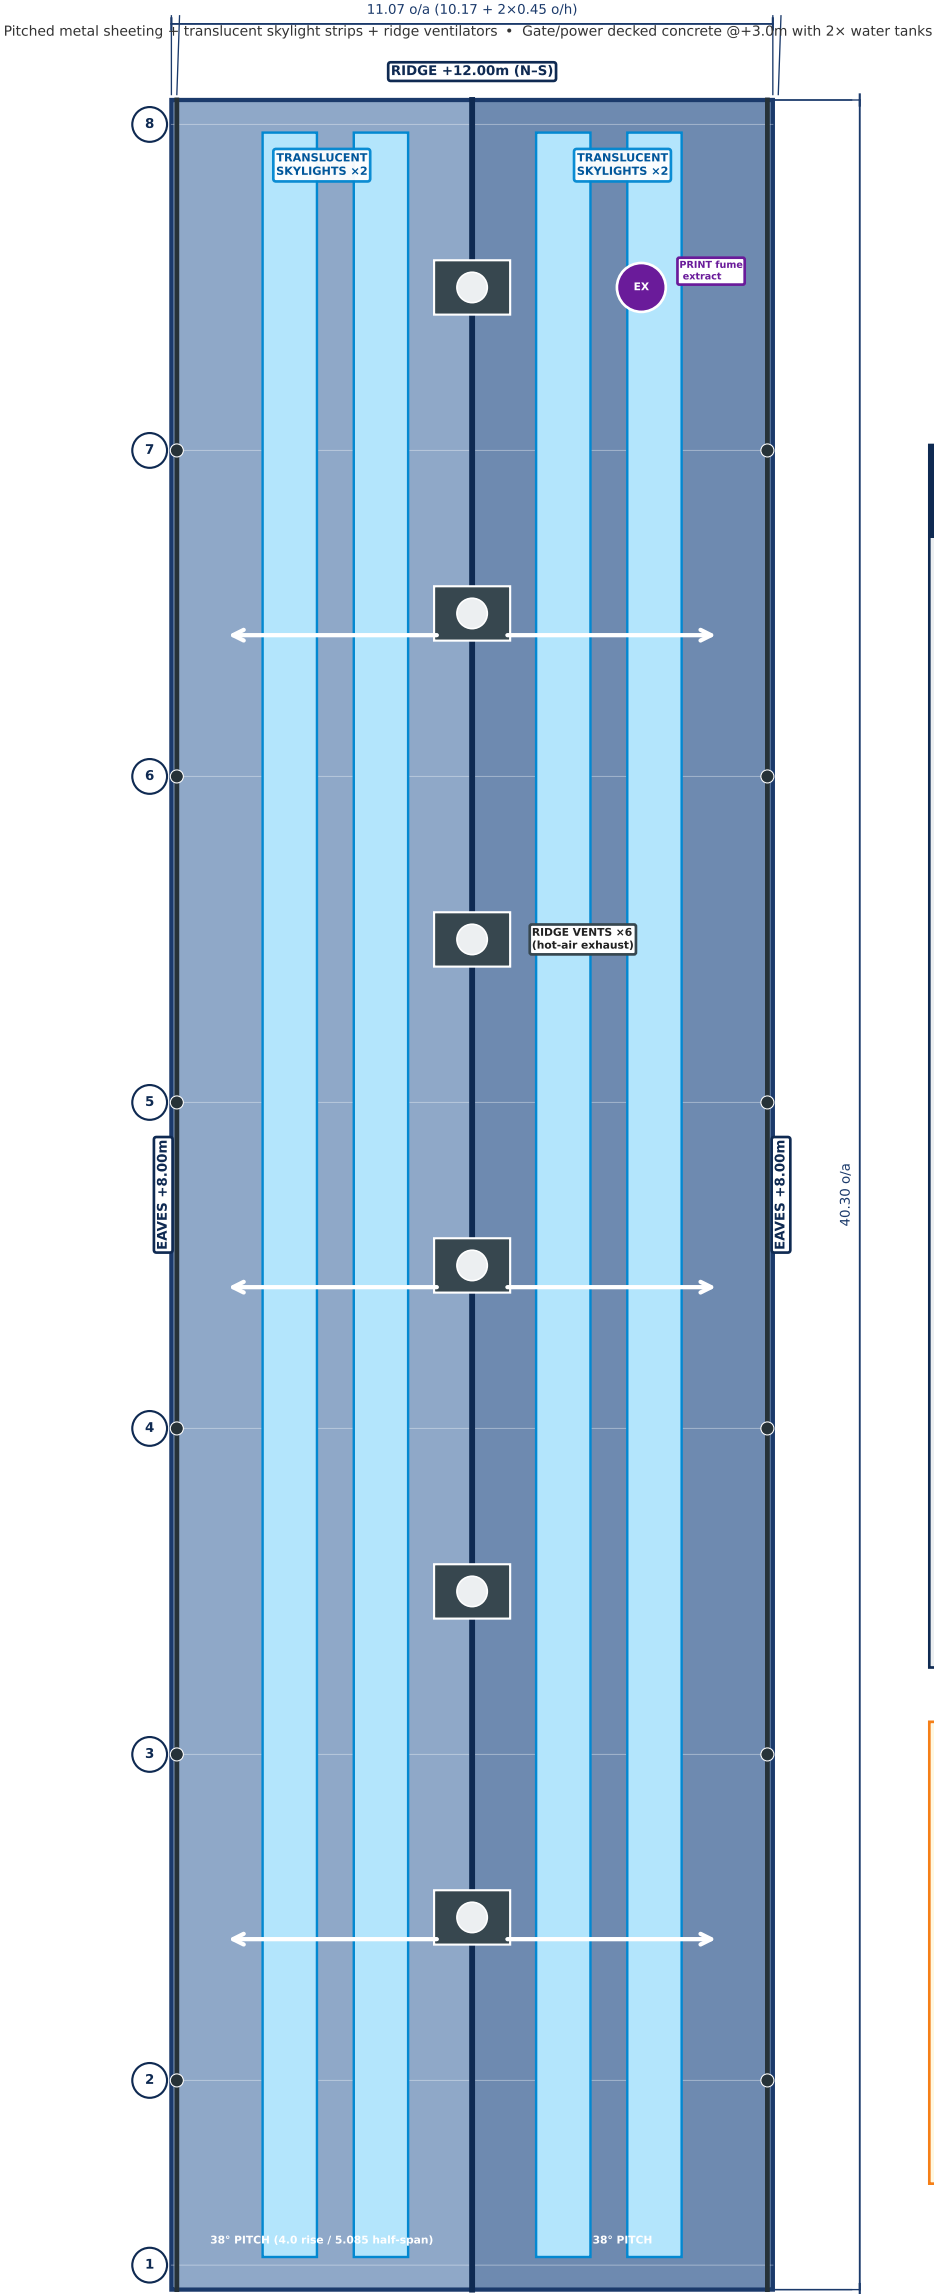

ROOF SPEC

- 0.55 aluminium-zinc metal sheeting, fixed to steel purlins.
- Pitch 38° (4.0/5.085).
- Skylights: translucent GRP/polycarbonate, 1.0 wide x2/slope.
- Ridge vents x6 + eaves gap vent.
- Gutters 150 uPVC + RWP @6m to soakaway.
- Purlins RHS + sag rods.
- Portal rafters UB/RSJ @6.0m (7 frames).
- Eaves HDG fascia.
- Print extract: 300Ø duct + cowl + fan.
- Lightning tape + rods.

DECK + TANKS

- Deck 150 RC + Falls.
- 2x 2000L water + header.
- Borehole → tanks → points (gravity).
- Overflow to drain.
- Parapet 450 + rail.
- Ladder access (E).

NYLON PRODUCTION & PACKAGING PLANT

Along Ilogbo / Foundation Road, Oko-Afo, Badagry LGA, Lagos State

A104 | ROOF PLAN • SKYLIGHTS + VENTS • GATE DECK + TANKS

1:100 | 27-09-2026

PRELIMINARY - FOR DISCUSSION